

Parts List

Item	Part Name	Material	Description
1	metal	~~Sh~~eet metal	~~Ma~~in metal sheet cutout
2	wood	Oak, Red	~~Wo~~od side and back panels
3	drip tray	~~Sh~~eet metal	~~Drip~~ tray
4	buttons	~~PL~~A	~~3D~~ printed
5	nozzle	~~PL~~A	~~3D~~ printed

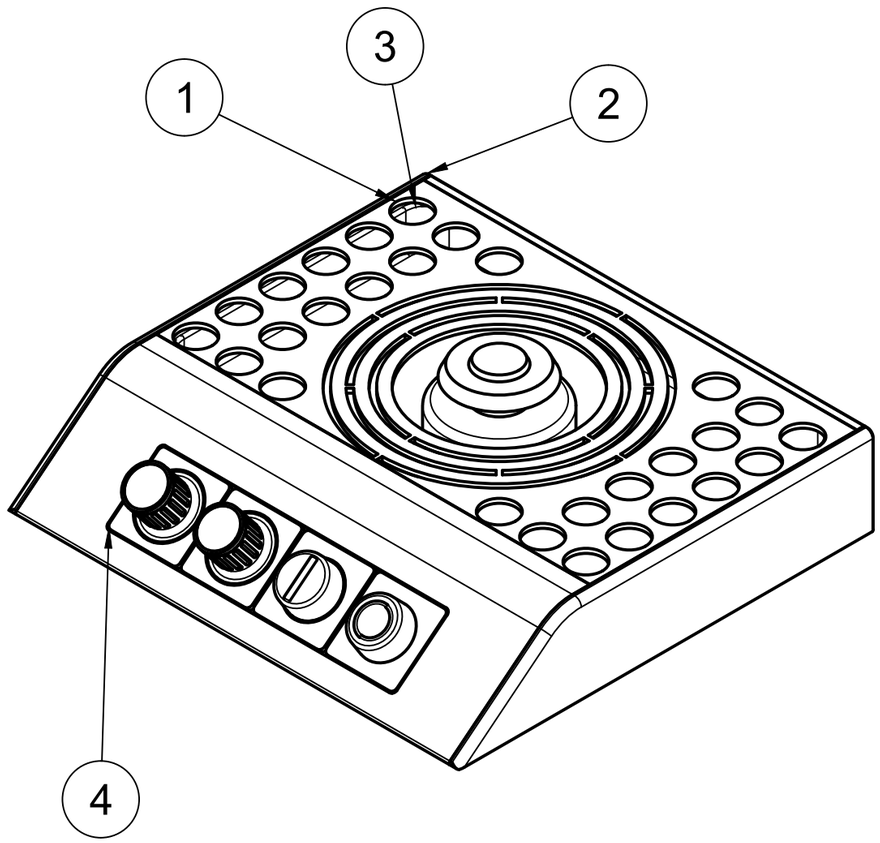

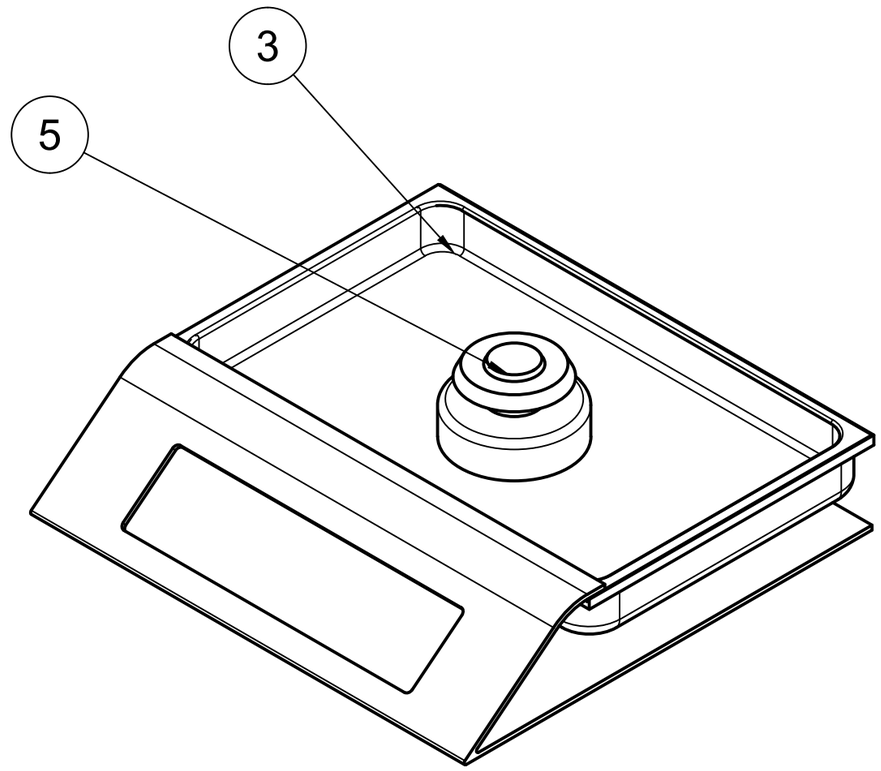

ISSUE DATE: 9/24/2024

REVISION: 1

UNIVERSITY OF CANTERBURY
Te Whare Wānanga o Waitaha
CHRISTCHURCH NEW ZEALAND

THE DESIGNS AND DETAILS SHOWN ARE COPYRIGHT AND MAY NOT BE USED FOR ANY PURPOSE WITHOUT PERMISSION OF THE SCHOOL OF PRODUCT DESIGN

COMPLETED IN ACCORDANCE WITH NZS/AS 1100.101:1992

CREATED BY: Kevin Chung

CHECKED / APPROVED BY:

DOCUMENT STATUS: In development

PROJECT TITLE: Bottom filling dispenser

DRAWING TITLE: Parts list

DRAWING NUMBER: 1


NOTES:

UNLESS OTHERWISE SPECIFIED: DIMENSIONS ARE IN MILLIMETERS


PAPER SIZE: A3


SCALE: 1:2

SHEET: 1/7

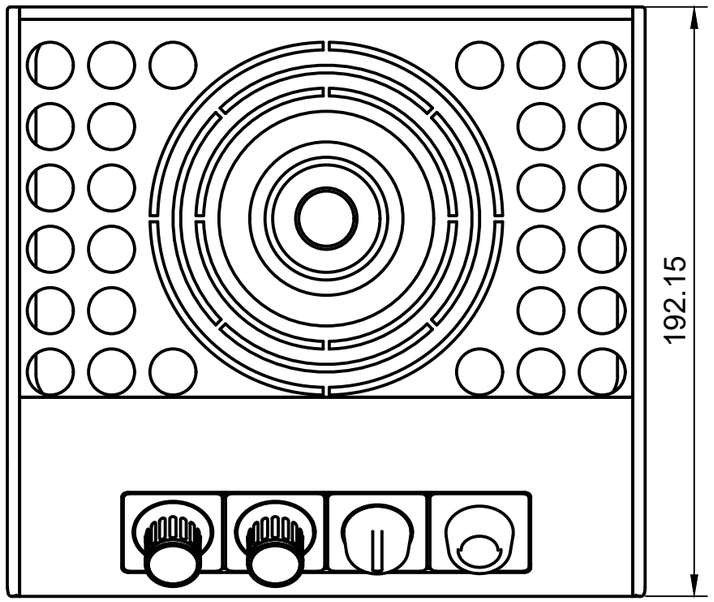



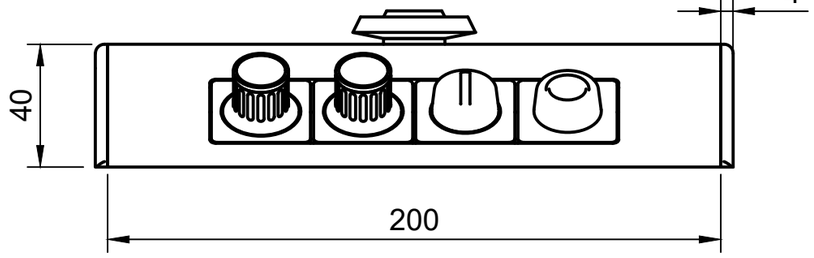

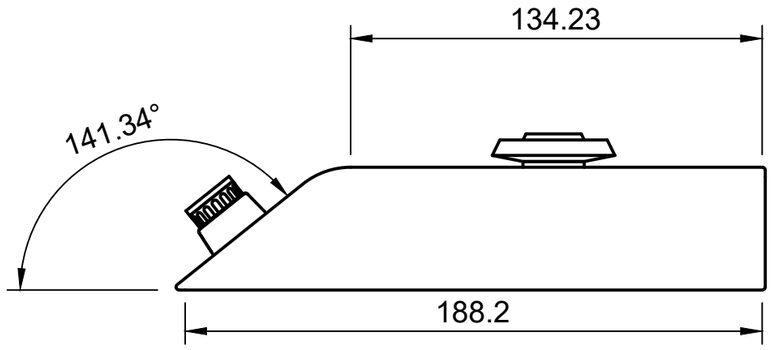

ISSUE DATE: 9/24/2024	REVISION: 1

UNIVERSITY OF CANTERBURY
Te Whare Wānanga o Waitaha
CHRISTCHURCH NEW ZEALAND

THE DESIGNS AND DETAILS SHOWN ARE COPYRIGHT AND MAY NOT BE USED FOR ANY PURPOSE WITHOUT PERMISSION OF THE SCHOOL OF PRODUCT DESIGN

COMPLETED IN ACCORDANCE WITH NZS/AS 1100.101:1992

CREATED BY:
Kevin Chung

CHECKED / APPROVED BY:

DOCUMENT STATUS:
In development

PROJECT TITLE:
Bottom filling dispenser

DRAWING TITLE:
General dimension


DRAWING NUMBER:
2


NOTES:


UNLESS OTHERWISE SPECIFIED: DIMENSIONS ARE IN MILLIMETERS

PAPER SIZE: A3

SCALE:	SHEET:
1:2	2/7

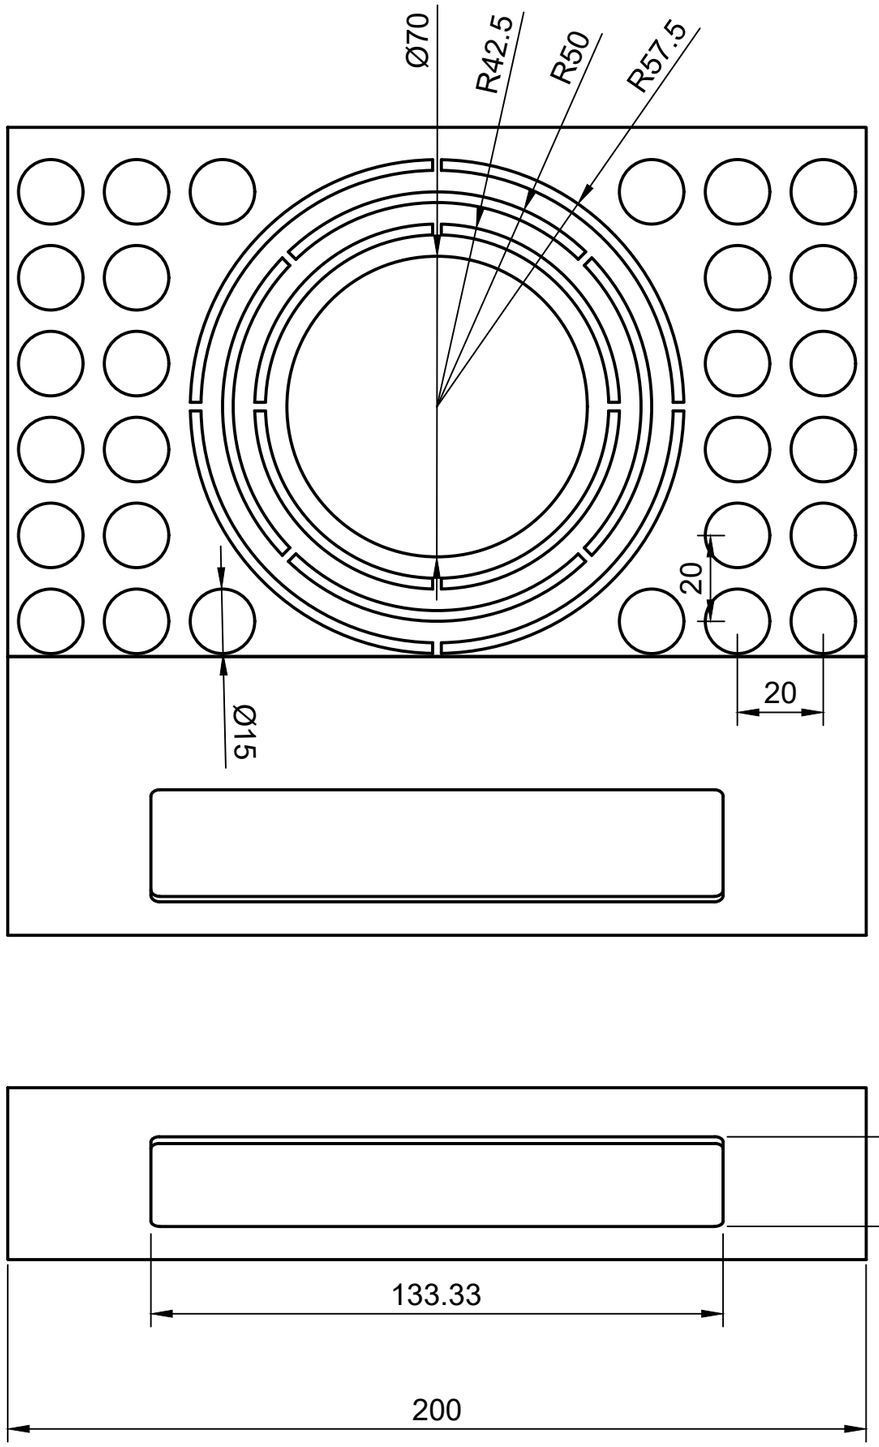

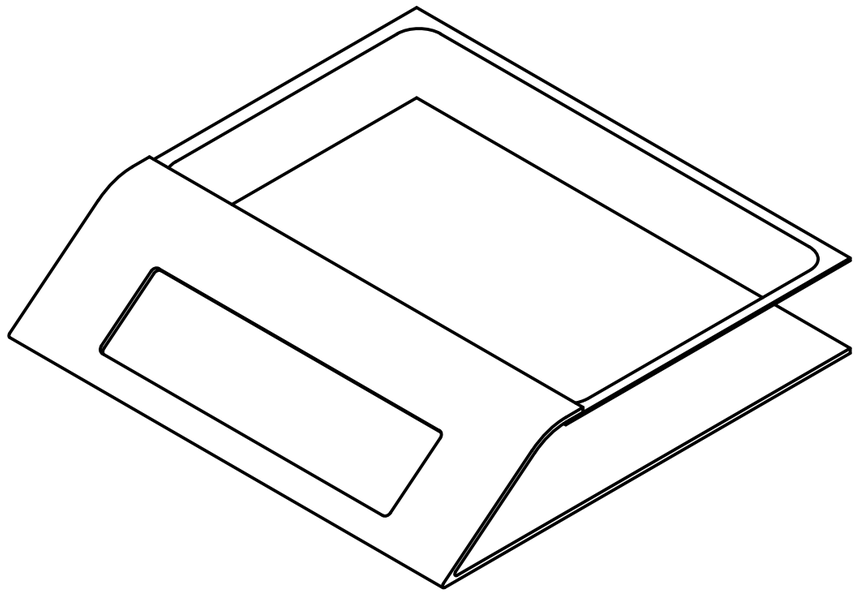

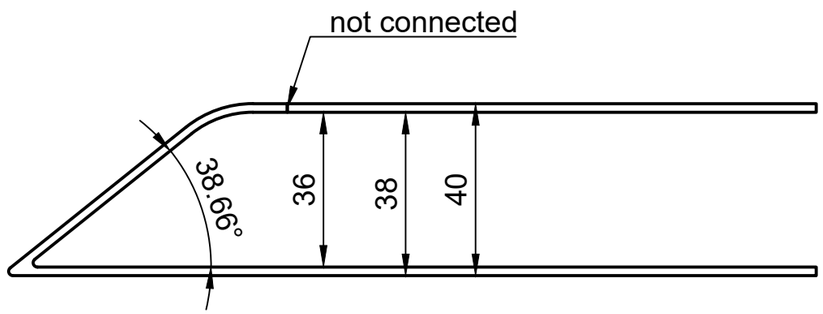

ISSUE DATE: 9/24/2024	REVISION: 1

UNIVERSITY OF CANTERBURY
Te Whare Wānanga o Waitaha
CHRISTCHURCH NEW ZEALAND

THE DESIGNS AND DETAILS SHOWN ARE COPYRIGHT AND MAY NOT BE USED FOR ANY PURPOSE WITHOUT PERMISSION OF THE SCHOOL OF PRODUCT DESIGN

COMPLETED IN ACCORDANCE WITH NZS/AS 1100.101:1992

CREATED BY: Kevin Chung

CHECKED / APPROVED BY:

DOCUMENT STATUS: In development

PROJECT TITLE: Bottom filling dispenser


DRAWING TITLE: sheet metal dimension


DRAWING NUMBER: 3


NOTES: the total length of the sheet metal including the channel drain is 400 mm

UNLESS OTHERWISE SPECIFIED: DIMENSIONS ARE IN MILLIMETERS

PAPER SIZE:	A3
SCALE: 7:10	SHEET: 3/7

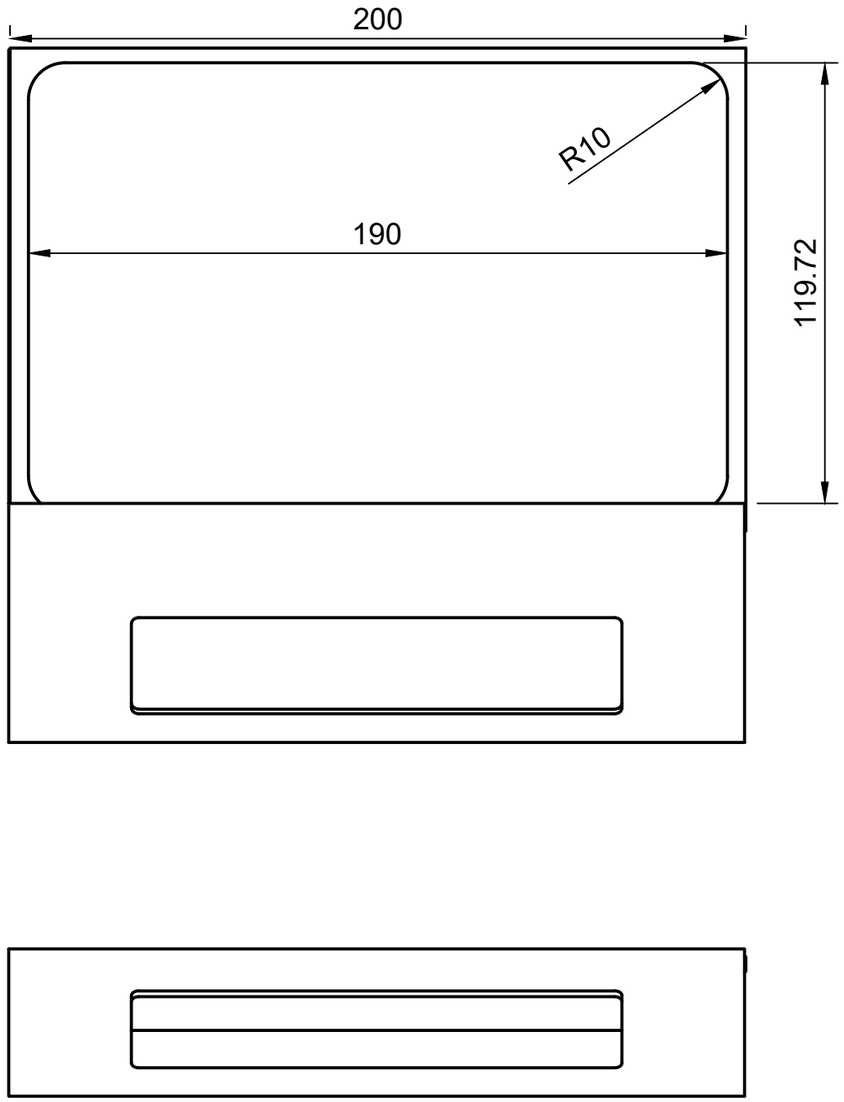

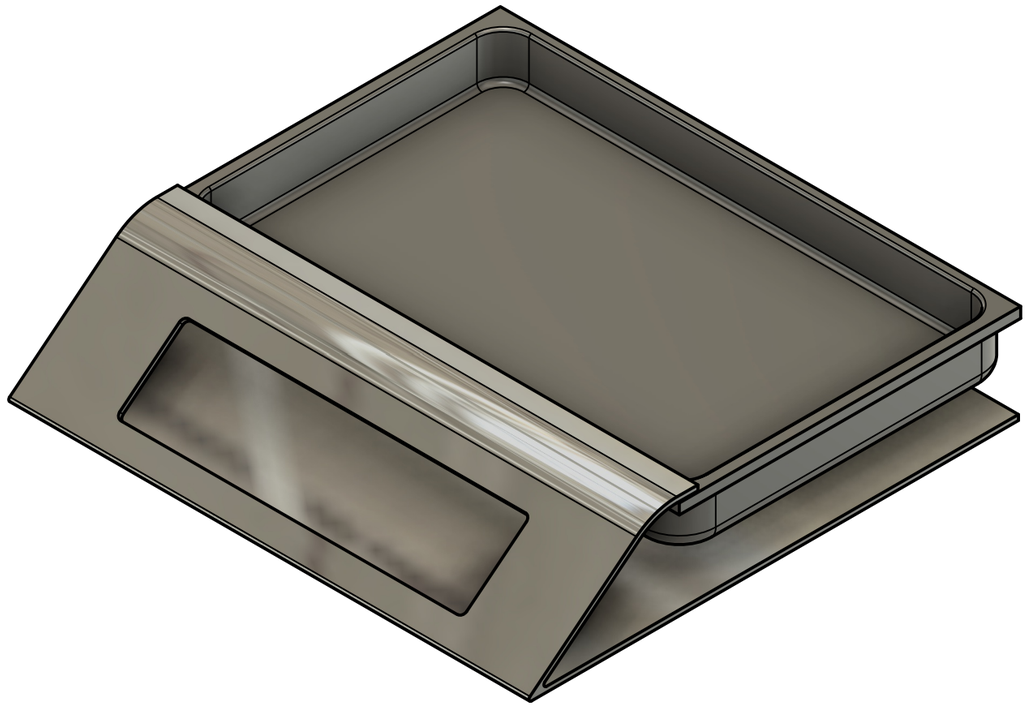

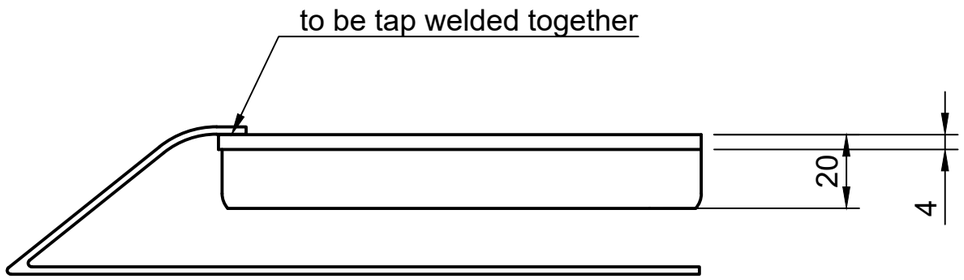

ISSUE DATE: 9/24/2024	REVISION: 1

UNIVERSITY OF CANTERBURY
Te Whare Wānanga o Waitaha
CHRISTCHURCH NEW ZEALAND

THE DESIGNS AND DETAILS SHOWN ARE COPYRIGHT AND MAY NOT BE USED FOR ANY PURPOSE WITHOUT PERMISSION OF THE SCHOOL OF PRODUCT DESIGN

COMPLETED IN ACCORDANCE WITH NZS/AS 1100.101:1992

CREATED BY:
Kevin Chung

CHECKED / APPROVED BY:

DOCUMENT STATUS:
In development

PROJECT TITLE:
Bottom filling dispenser


DRAWING TITLE:
Drip Tray Dimension


DRAWING NUMBER:
4


NOTES:
The drip tray is to be tap welded onto the main sheet metal


UNLESS OTHERWISE SPECIFIED: DIMENSIONS ARE IN MILLIMETERS

PAPER SIZE:	A3
SCALE: 3:5	SHEET: 4/7

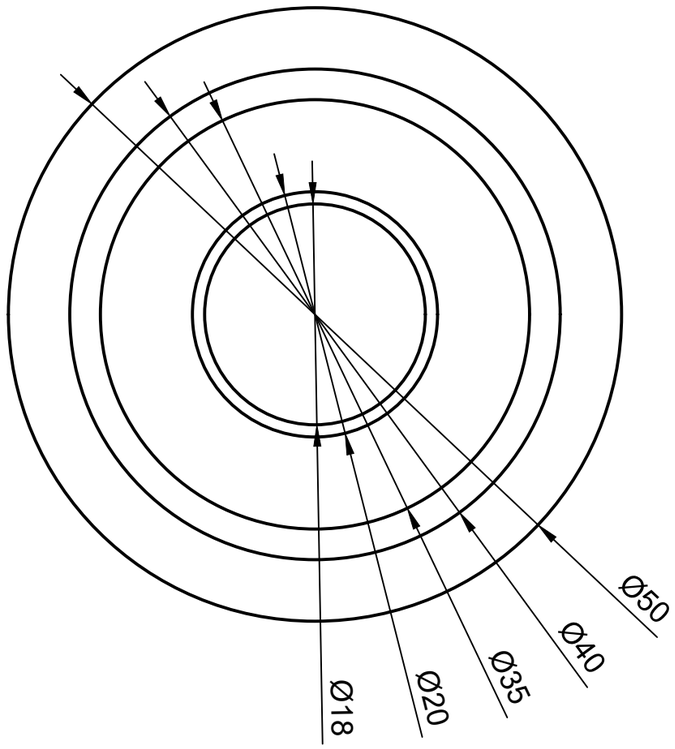

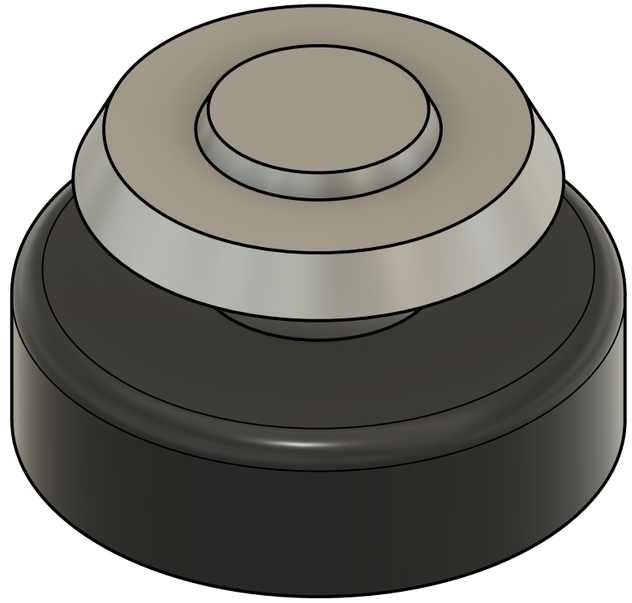

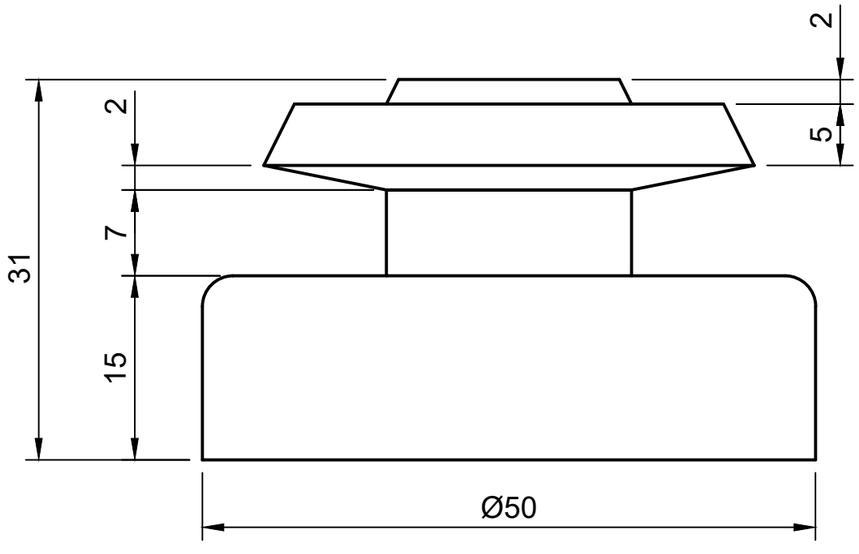

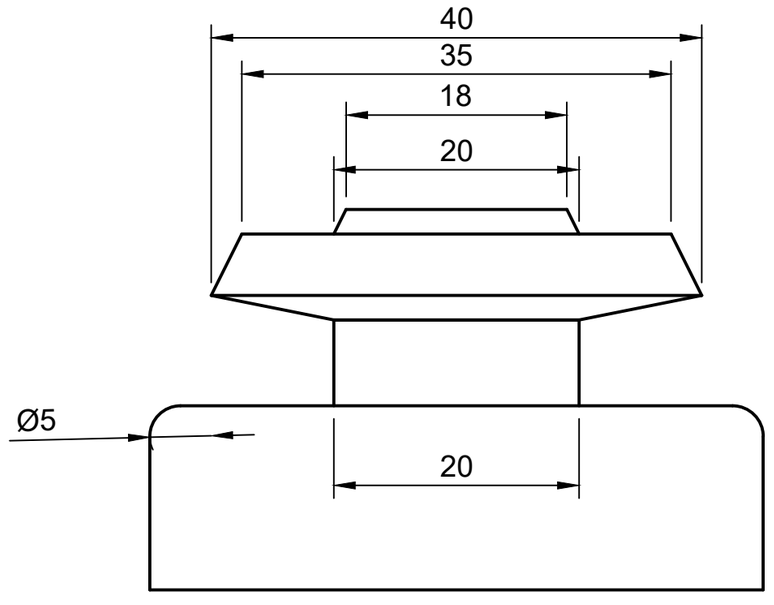

ISSUE DATE: 9/24/2024	REVISION: 1

UNIVERSITY OF CANTERBURY
Te Whare Wānanga o Waitaha
CHRISTCHURCH NEW ZEALAND

THE DESIGNS AND DETAILS SHOWN ARE COPYRIGHT AND MAY NOT BE USED FOR ANY PURPOSE WITHOUT PERMISSION OF THE SCHOOL OF PRODUCT DESIGN

COMPLETED IN ACCORDANCE WITH NZS/AS 1100.101:1992

CREATED BY:
Kevin Chung
CHECKED / APPROVED BY:

DOCUMENT STATUS:
In development

PROJECT TITLE:
Bottom Filling Dispenser


DRAWING TITLE:
Nozzle dimensions


DRAWING NUMBER:
5


NOTES:
To be 3D printed


UNLESS OTHERWISE SPECIFIED: DIMENSIONS ARE IN MILLIMETERS

PAPER SIZE:	A3
SCALE: 2	SHEET: 5/7

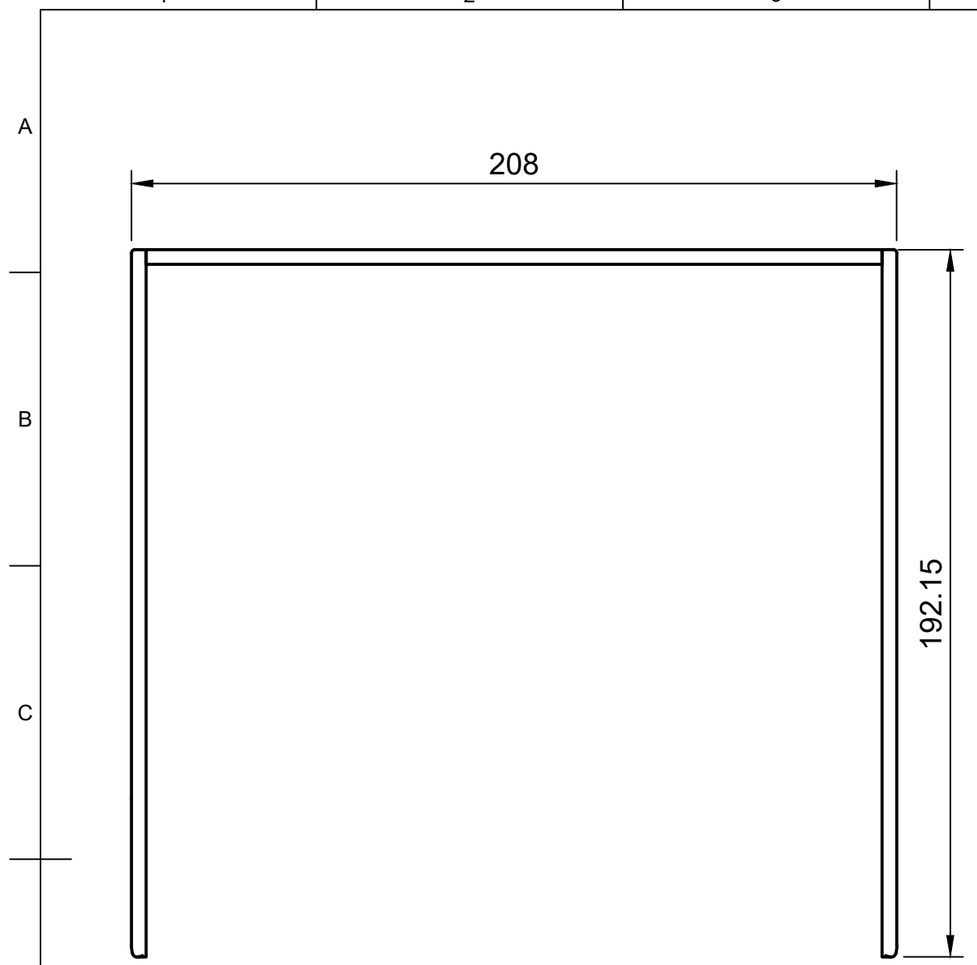

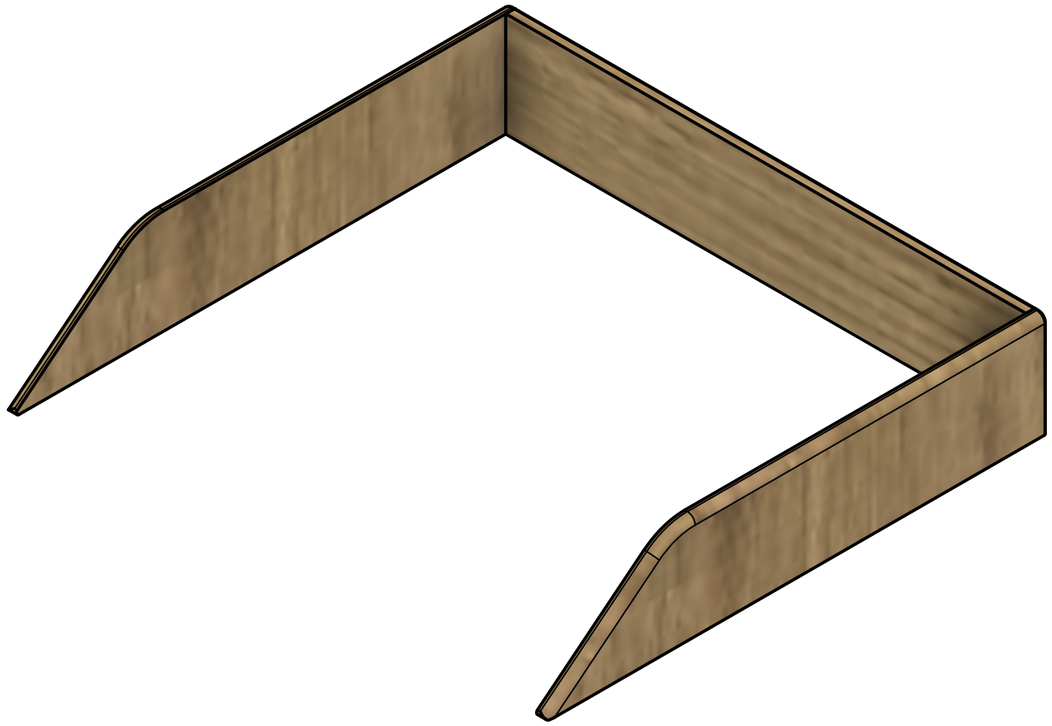

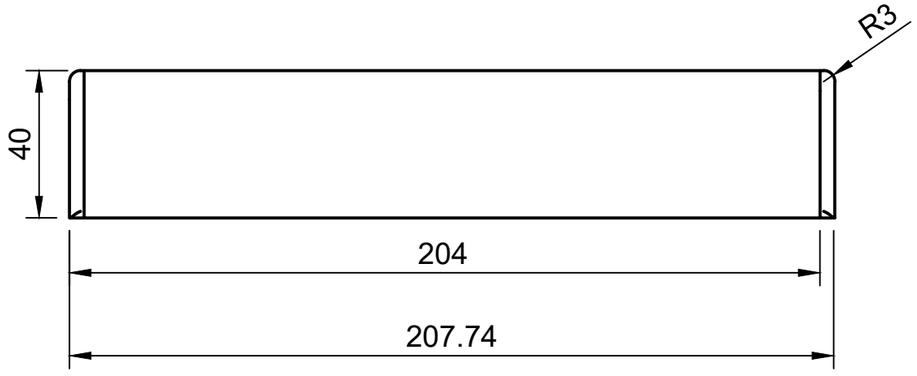

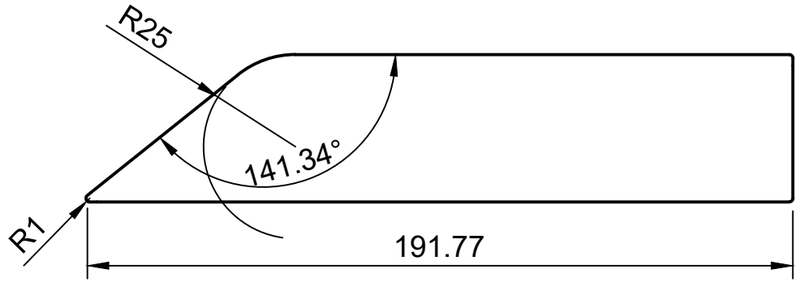

ISSUE DATE: 9/24/2024	REVISION: 1

UNIVERSITY OF CANTERBURY
Te Whare Wānanga o Waitaha
CHRISTCHURCH NEW ZEALAND

THE DESIGNS AND DETAILS SHOWN ARE COPYRIGHT AND MAY NOT BE USED FOR ANY PURPOSE WITHOUT PERMISSION OF THE SCHOOL OF PRODUCT DESIGN

COMPLETED IN ACCORDANCE WITH NZS/AS 1100.101:1992

CREATED BY:
Kevin Chung

CHECKED / APPROVED BY:

DOCUMENT STATUS:
Kevin Chung

PROJECT TITLE:
Kevin Chung

DRAWING TITLE:
Kevin Chung


DRAWING NUMBER:
Kevin Chung


NOTES:
Kevin Chung


UNLESS OTHERWISE SPECIFIED: DIMENSIONS ARE IN MILLIMETERS


PAPER SIZE: A3


SCALE: 6:10	SHEET: 6/7

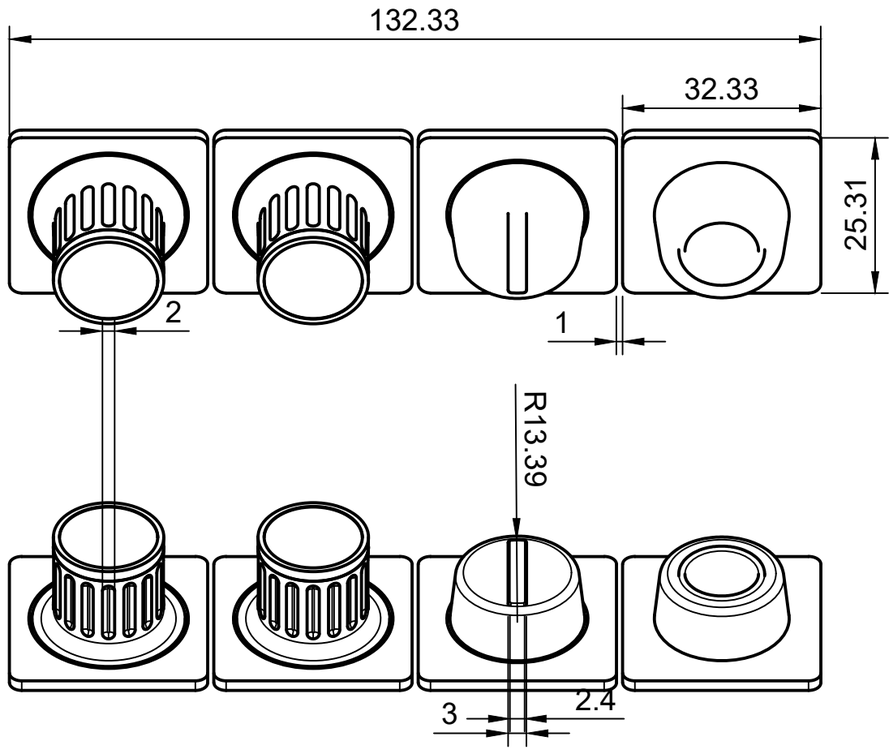

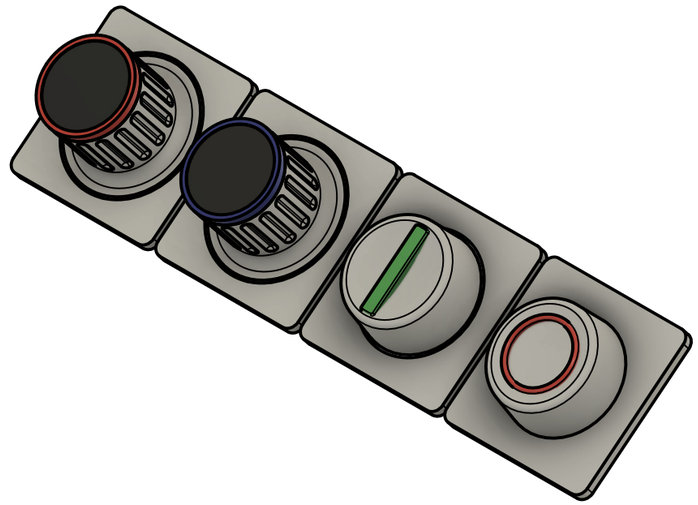

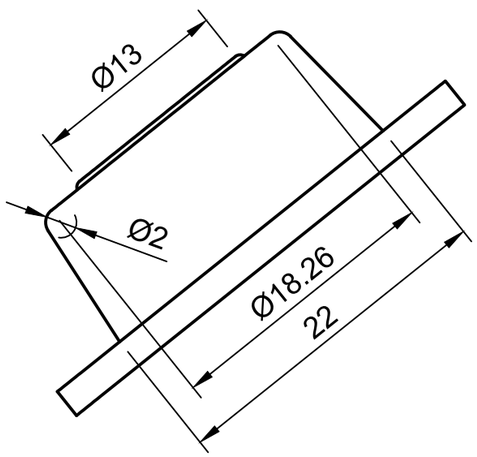

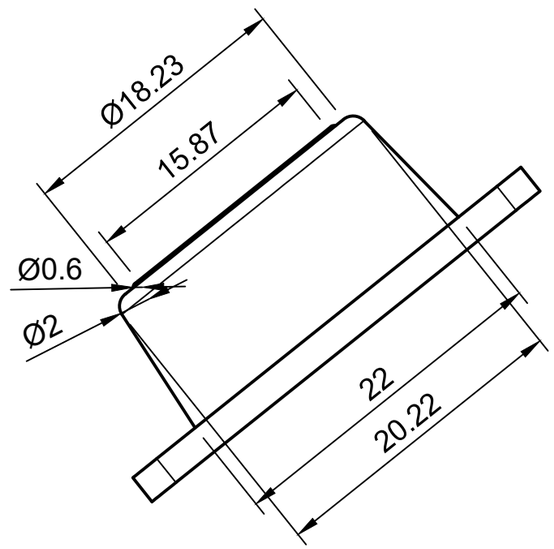

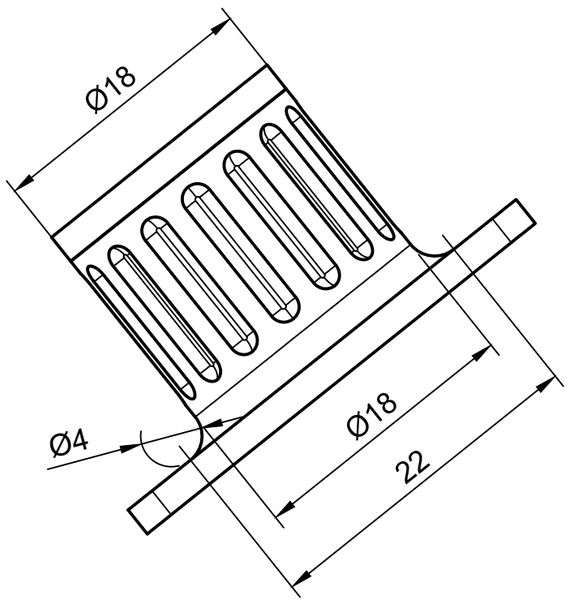

ISSUE DATE: 9/24/2024	REVISION: 1

UNIVERSITY OF CANTERBURY
Te Whare Wānanga o Waitaha
CHRISTCHURCH NEW ZEALAND

THE DESIGNS AND DETAILS SHOWN ARE COPYRIGHT AND MAY NOT BE USED FOR ANY PURPOSE WITHOUT PERMISSION OF THE SCHOOL OF PRODUCT DESIGN

COMPLETED IN ACCORDANCE WITH NZS/AS 1100.101:1992

CREATED BY:
Kevin Chung
CHECKED / APPROVED BY:

DOCUMENT STATUS:
In development

PROJECT TITLE:
Bottom Filling Dispenser

DRAWING TITLE:
Buttons dimensions

DRAWING NUMBER:
7

NOTES:
to be 3D printed

UNLESS OTHERWISE SPECIFIED: DIMENSIONS ARE IN MILLIMETERS

PAPER SIZE: A3	
SCALE: 1	SHEET: 7/7